


R1

緊急出口位置圖

Evacuation Plan

-  緊急出口
Emergency Exit
-  逃生方向
Escape Directions
-  消防栓
Fire Hydrant
-  滅火器
Fire Extinguisher

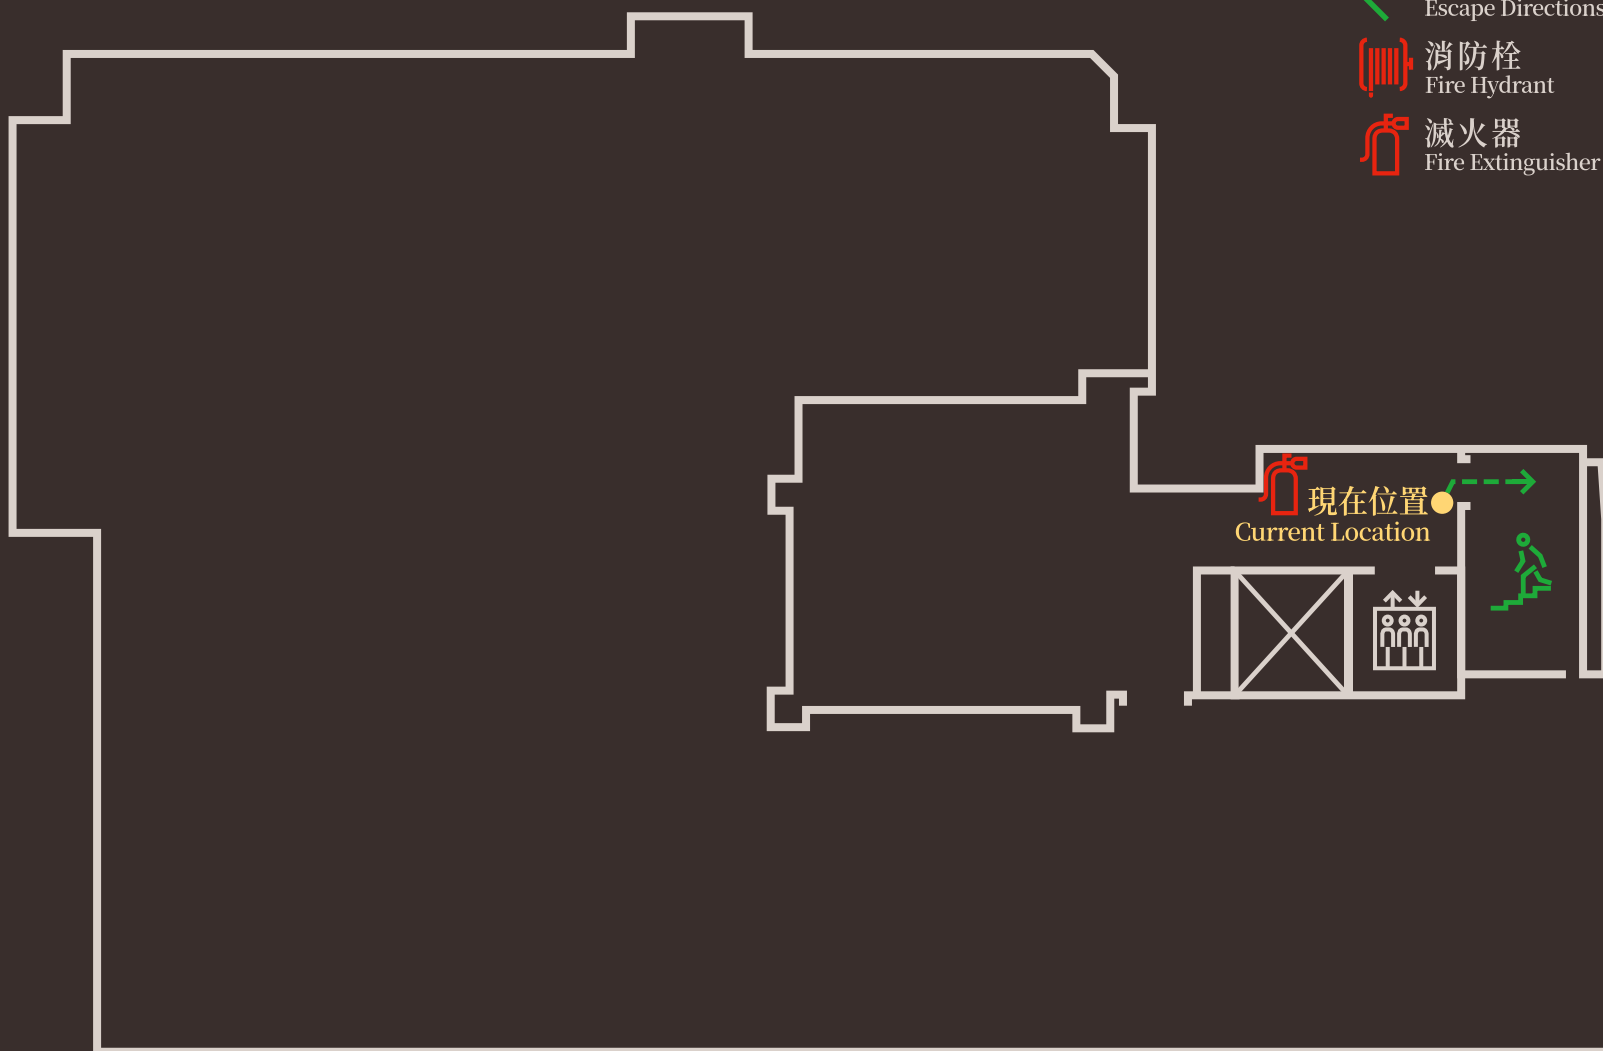


15F

緊急出口位置圖

Evacuation Plan

-  緊急出口
Emergency Exit
-  逃生方向
Escape Directions
-  消防栓
Fire Hydrant
-  滅火器
Fire Extinguisher

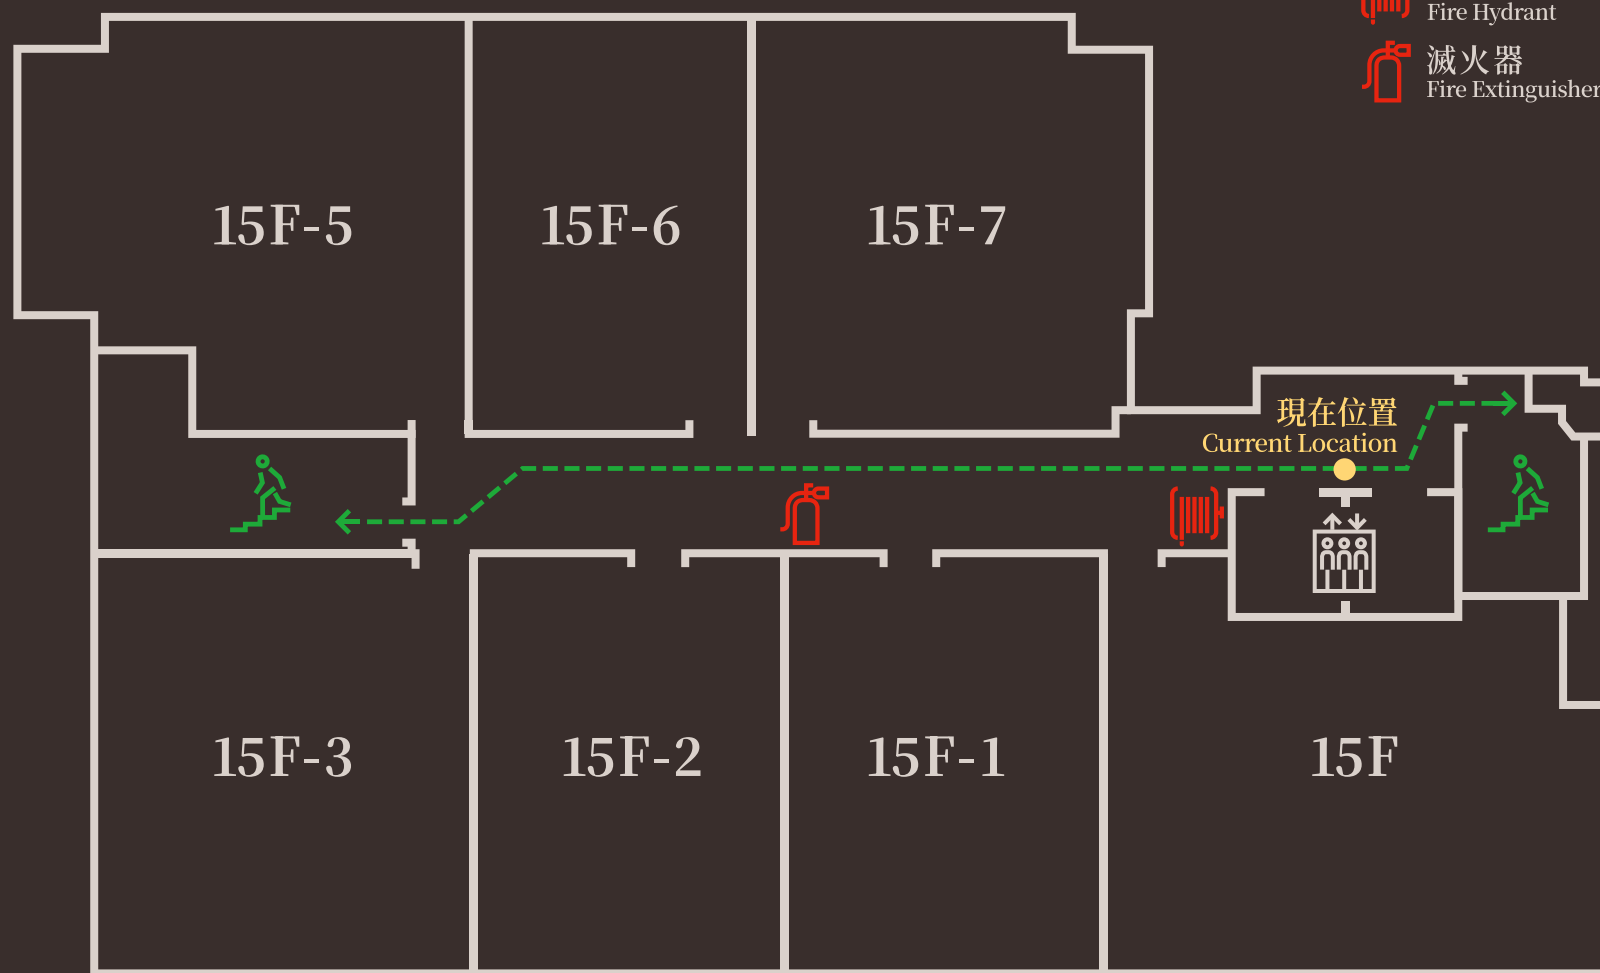


14F

緊急出口位置圖

Evacuation Plan

-  緊急出口
Emergency Exit
-  逃生方向
Escape Directions
-  消防栓
Fire Hydrant
-  滅火器
Fire Extinguisher

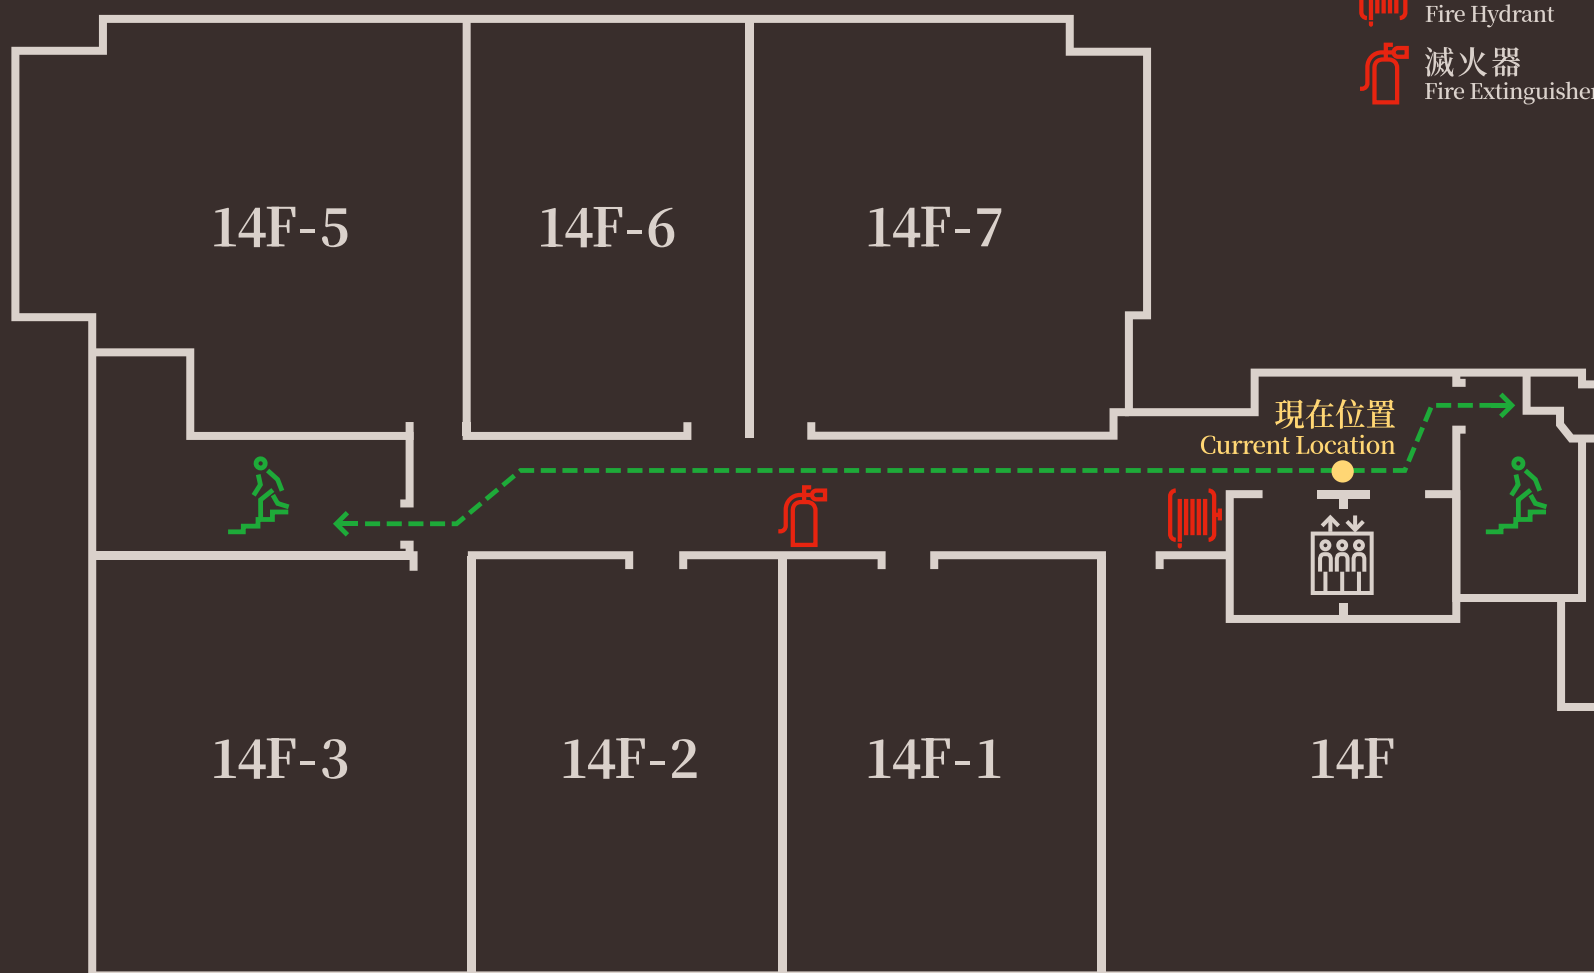


13F

緊急出口位置圖

Evacuation Plan

-  緊急出口
Emergency Exit
-  逃生方向
Escape Directions
-  消防栓
Fire Hydrant
-  滅火器
Fire Extinguisher

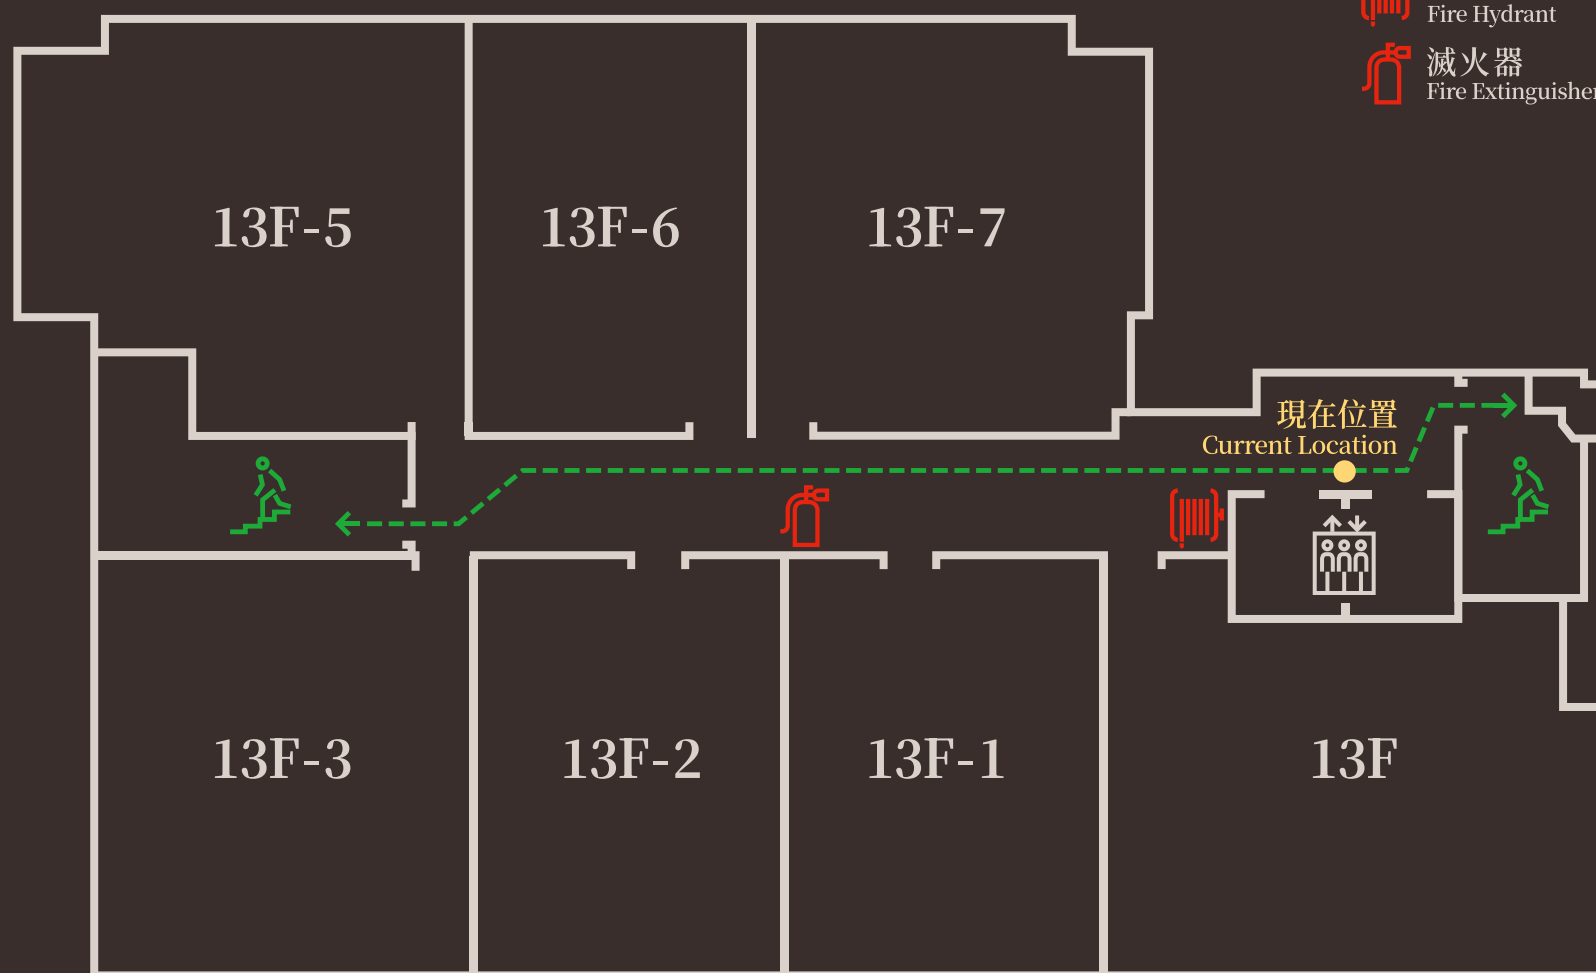


12F

緊急出口位置圖

Evacuation Plan

-  緊急出口
Emergency Exit
-  逃生方向
Escape Directions
-  消防栓
Fire Hydrant
-  滅火器
Fire Extinguisher

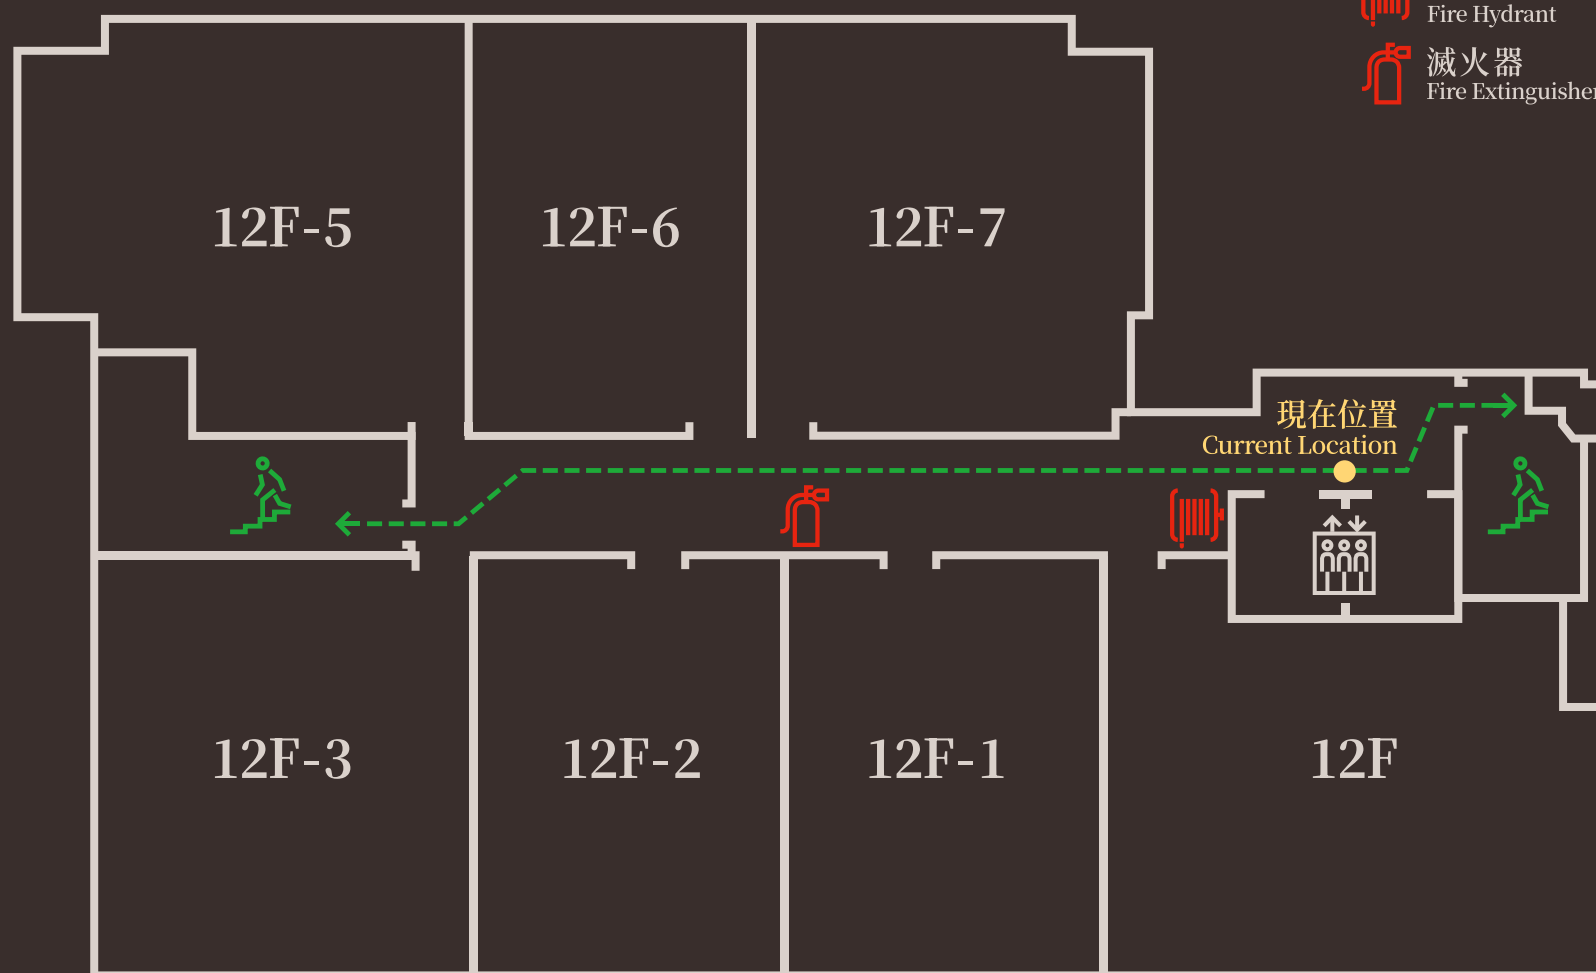


11F

緊急出口位置圖

Evacuation Plan

-  緊急出口
Emergency Exit
-  逃生方向
Escape Directions
-  消防栓
Fire Hydrant
-  滅火器
Fire Extinguisher

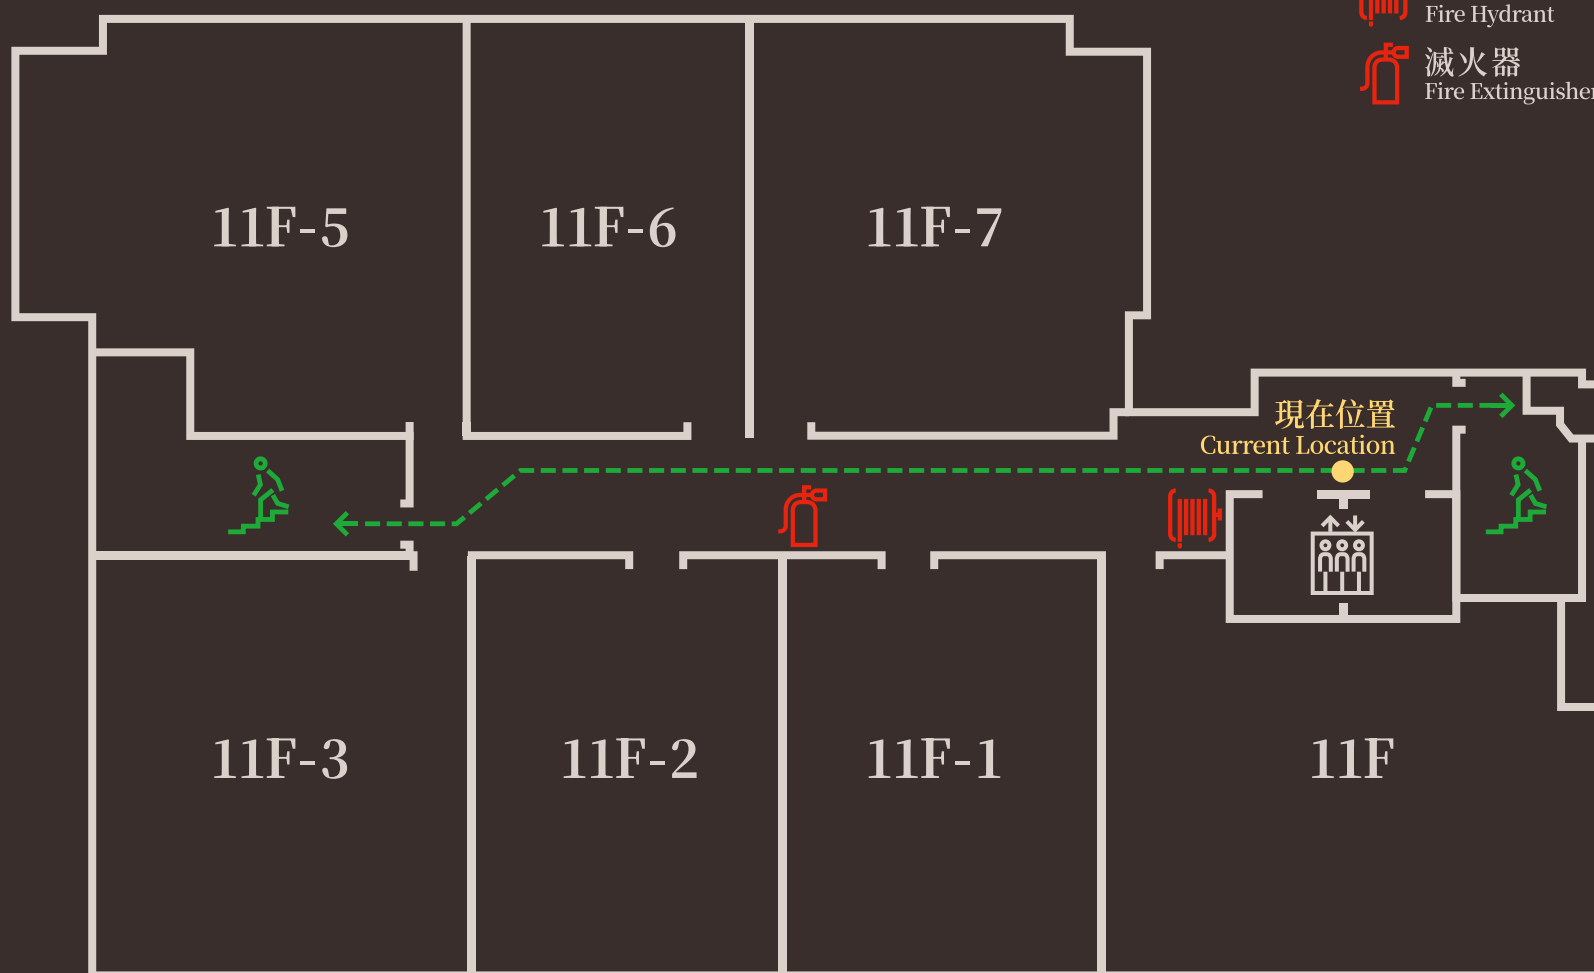


10F

緊急出口位置圖

Evacuation Plan

-  緊急出口
Emergency Exit
-  逃生方向
Escape Directions
-  消防栓
Fire Hydrant
-  滅火器
Fire Extinguisher

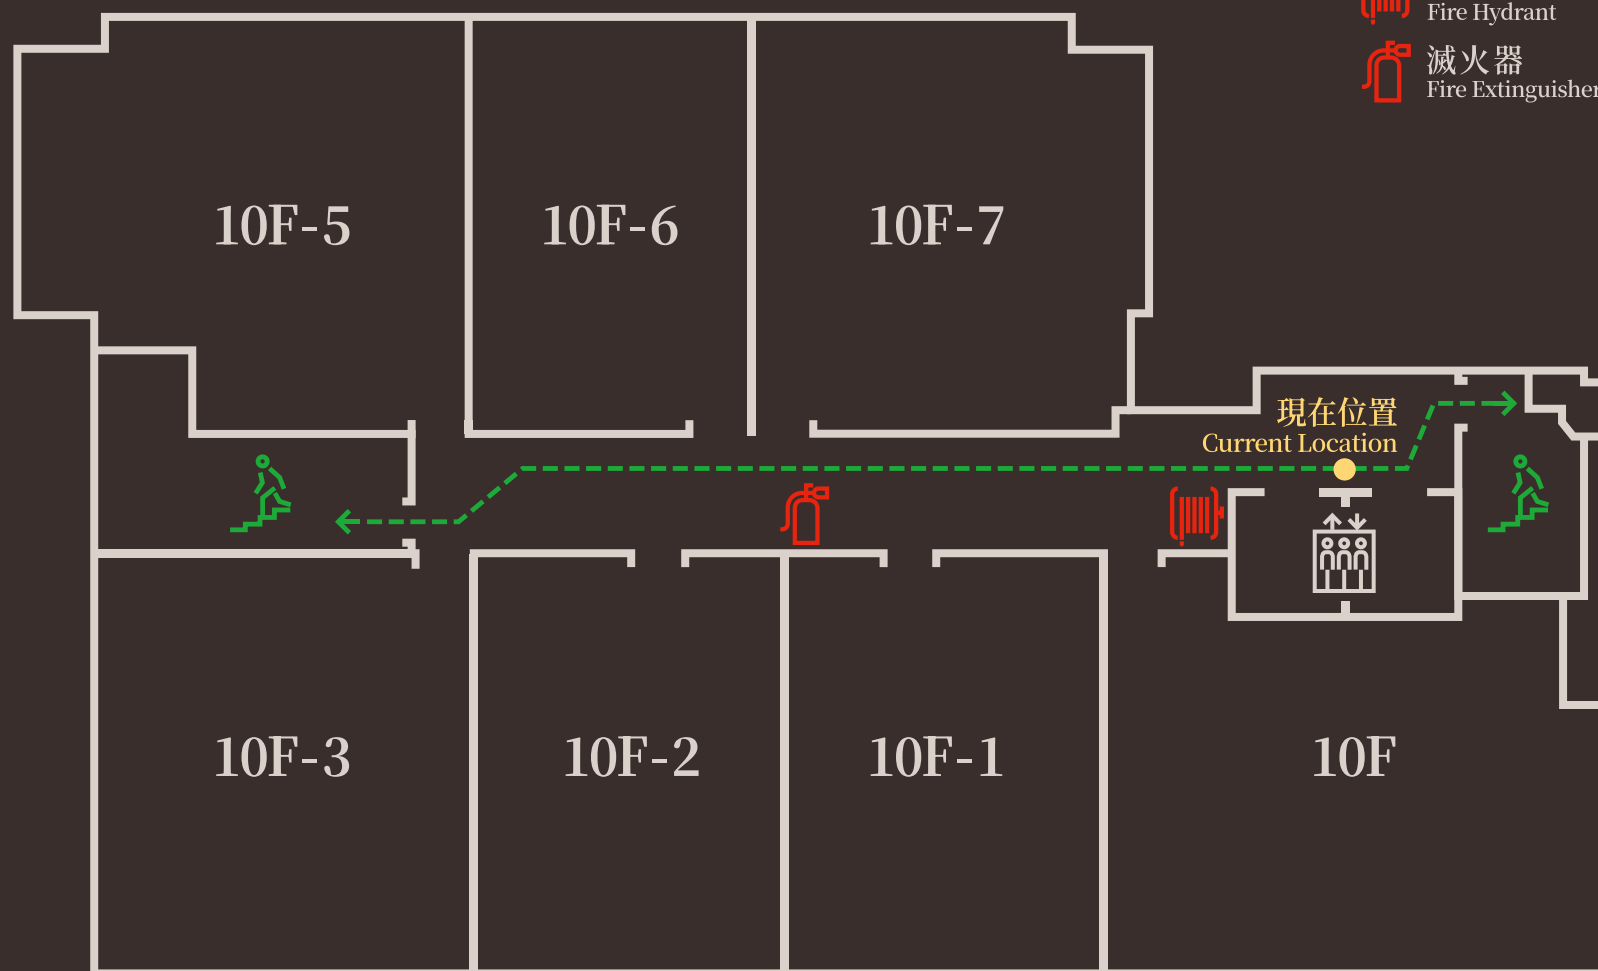


9F

緊急出口位置圖

Evacuation Plan

-  緊急出口
Emergency Exit
-  逃生方向
Escape Directions
-  消防栓
Fire Hydrant
-  滅火器
Fire Extinguisher

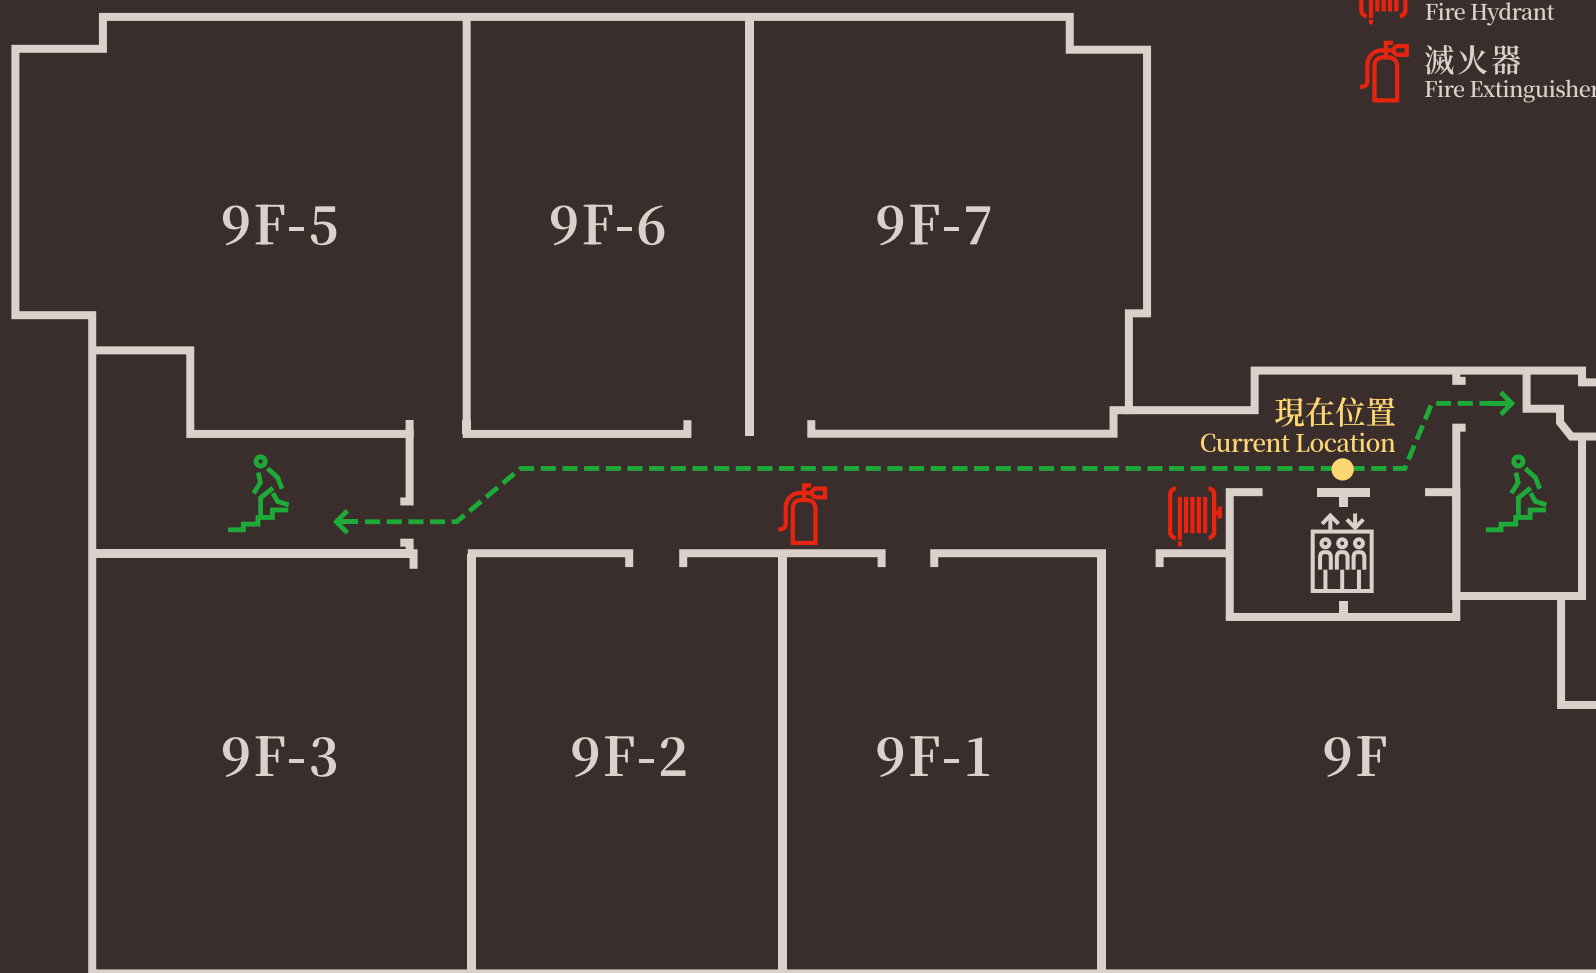


8F

緊急出口位置圖

Evacuation Plan

-  緊急出口
Emergency Exit
-  逃生方向
Escape Directions
-  消防栓
Fire Hydrant
-  滅火器
Fire Extinguisher

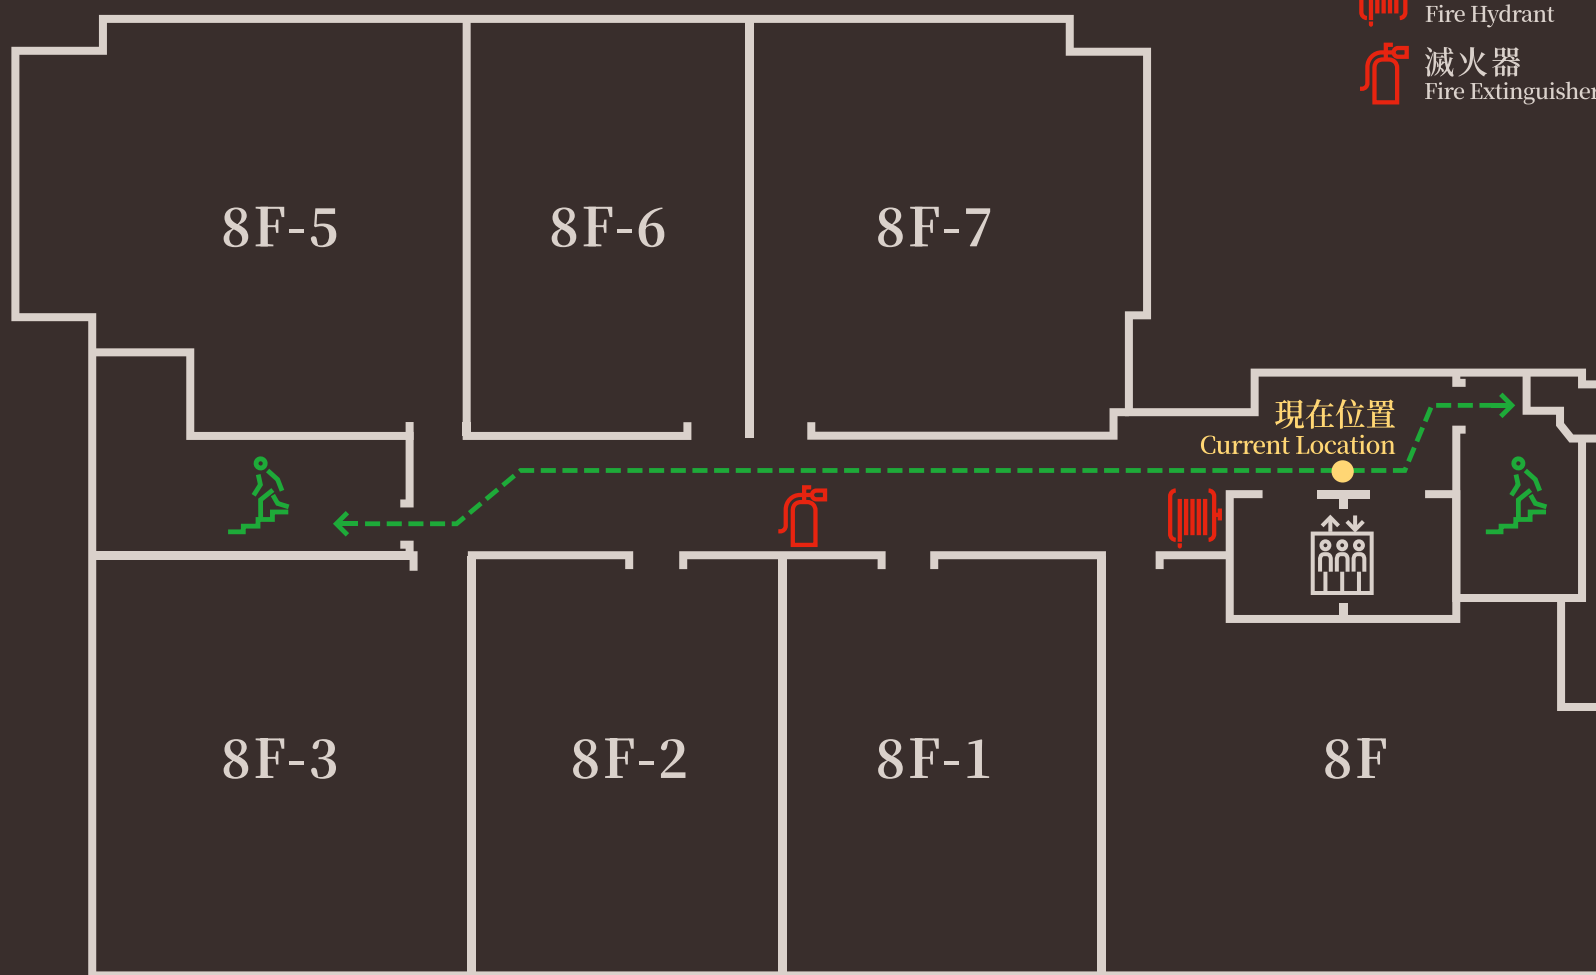

7F

緊急出口位置圖
Evacuation Plan

-  緊急出口
Emergency Exit
-  逃生方向
Escape Directions
-  消防栓
Fire Hydrant
-  滅火器
Fire Extinguisher




6F

緊急出口位置圖

Evacuation Plan

-  緊急出口
Emergency Exit
-  逃生方向
Escape Directions
-  消防栓
Fire Hydrant
-  滅火器
Fire Extinguisher

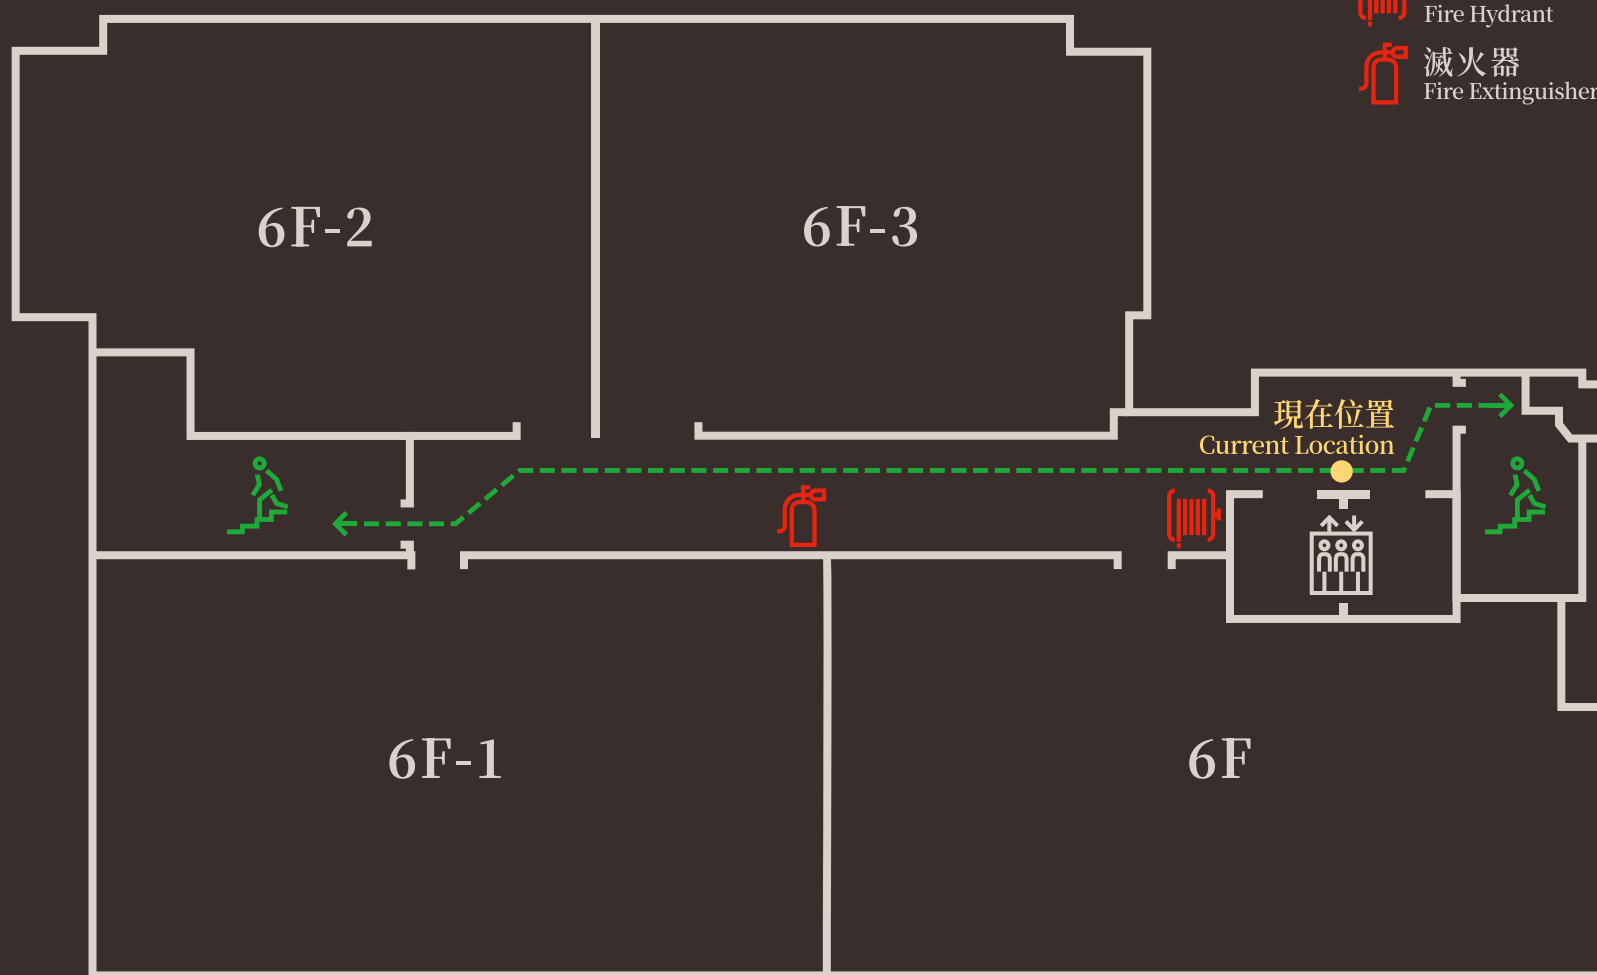


5F

緊急出口位置圖

Evacuation Plan

-  緊急出口
Emergency Exit
-  逃生方向
Escape Directions
-  消防栓
Fire Hydrant
-  滅火器
Fire Extinguisher

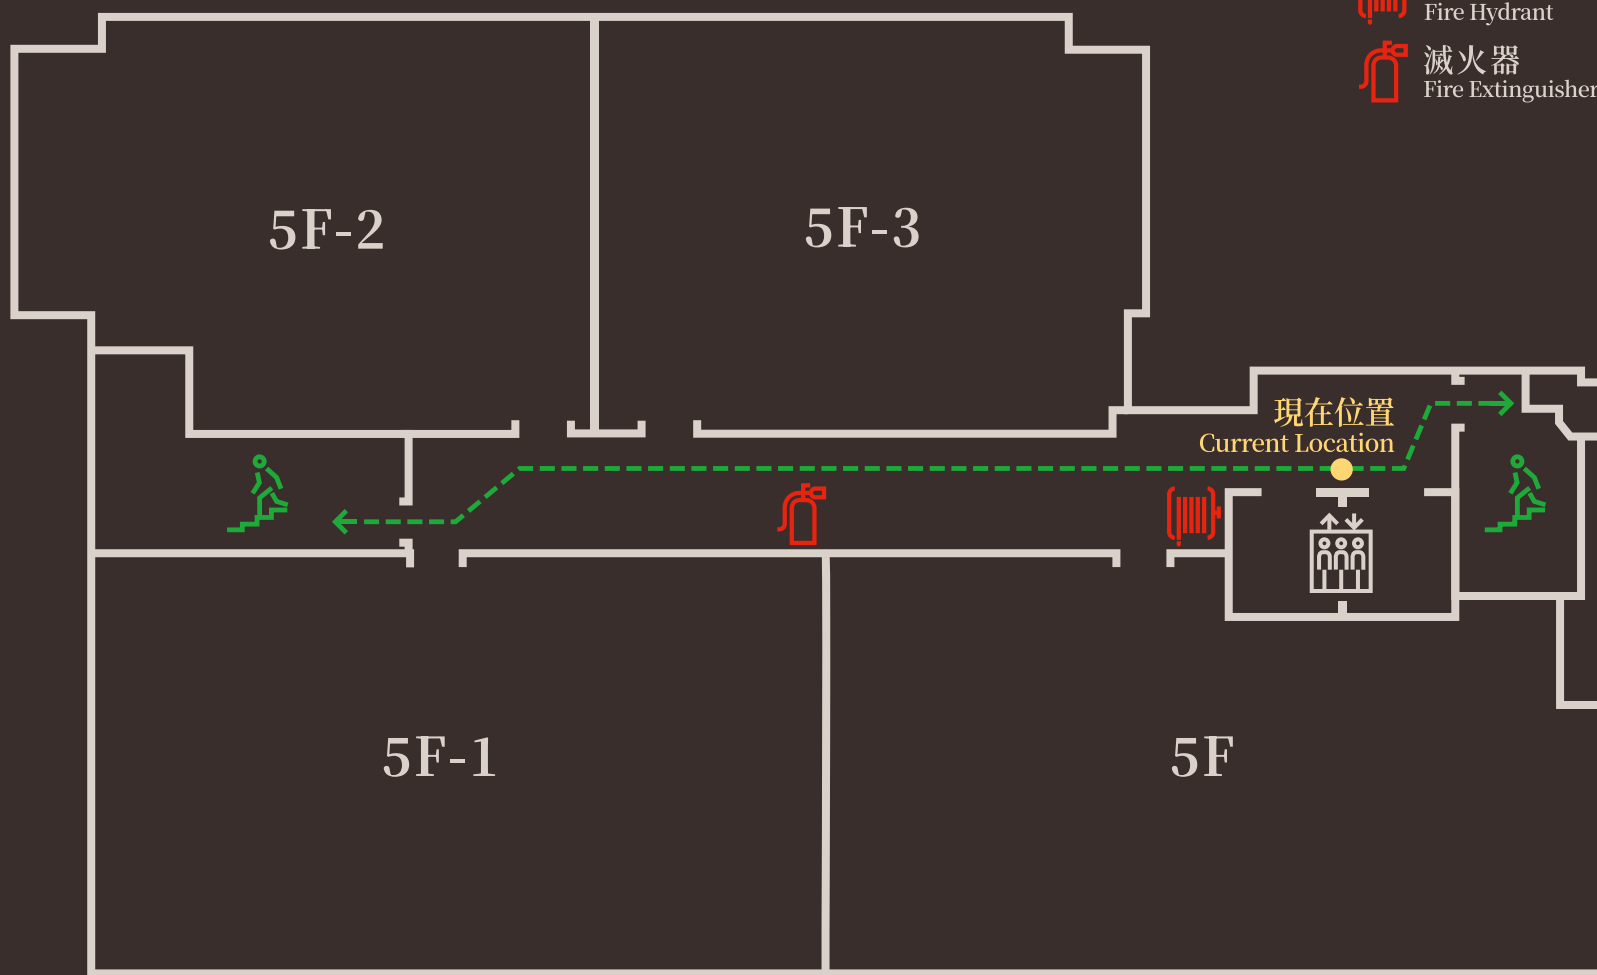


4F

緊急出口位置圖

Evacuation Plan

-  緊急出口
Emergency Exit
-  逃生方向
Escape Directions
-  消防栓
Fire Hydrant
-  滅火器
Fire Extinguisher

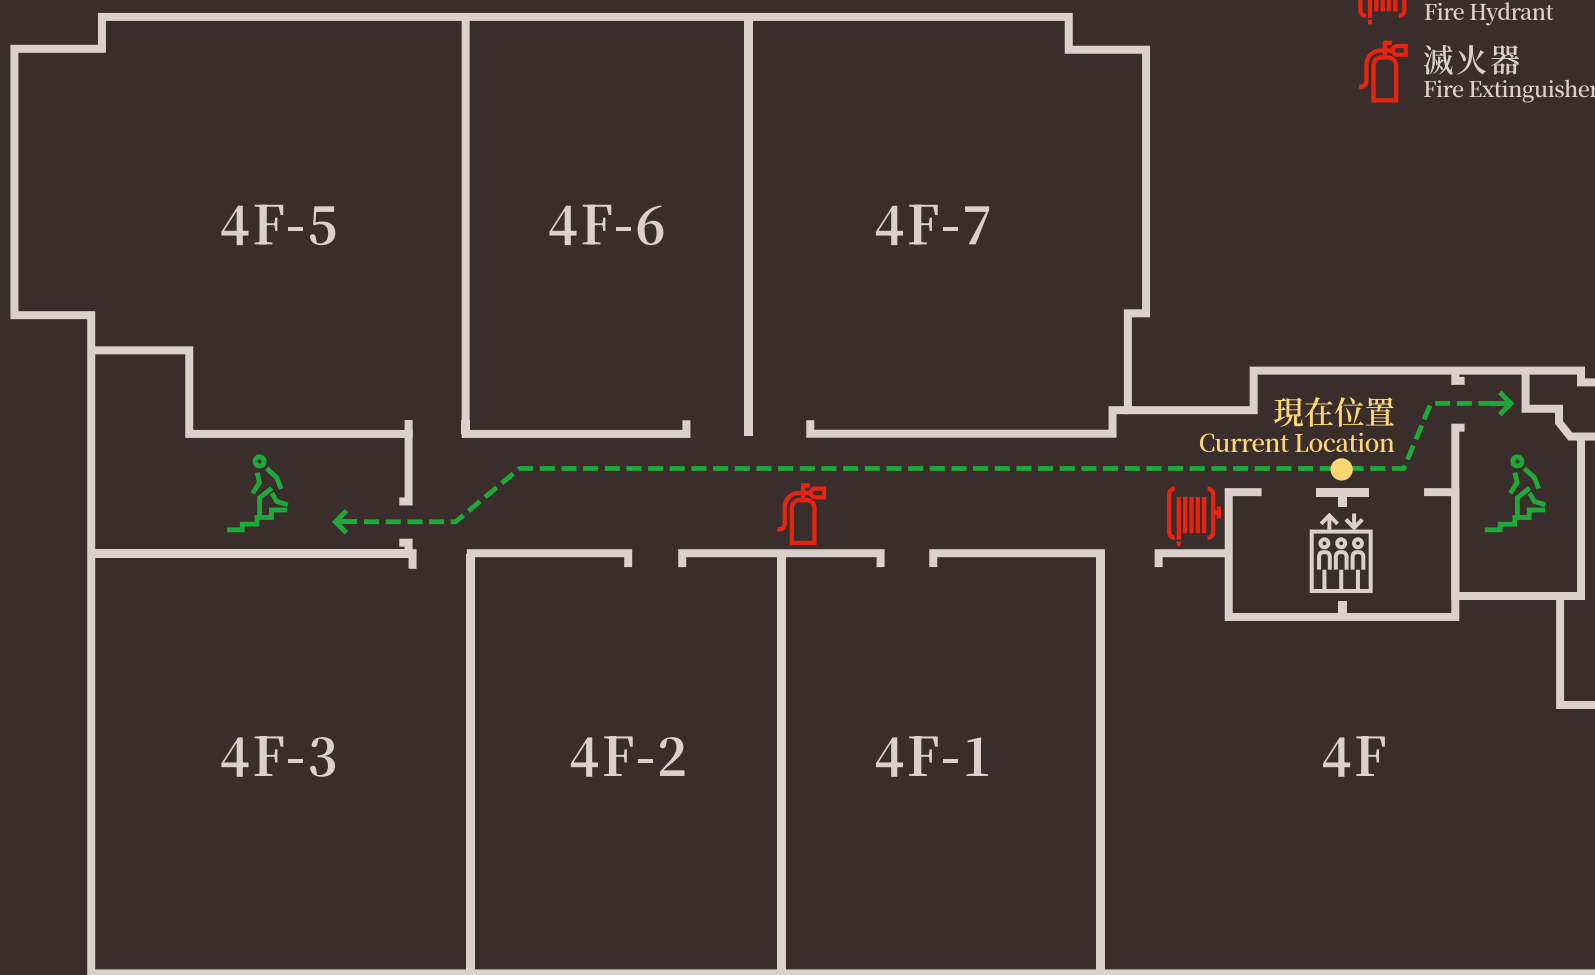


3F

緊急出口位置圖

Evacuation Plan

-  緊急出口
Emergency Exit
-  逃生方向
Escape Directions
-  消防栓
Fire Hydrant
-  滅火器
Fire Extinguisher

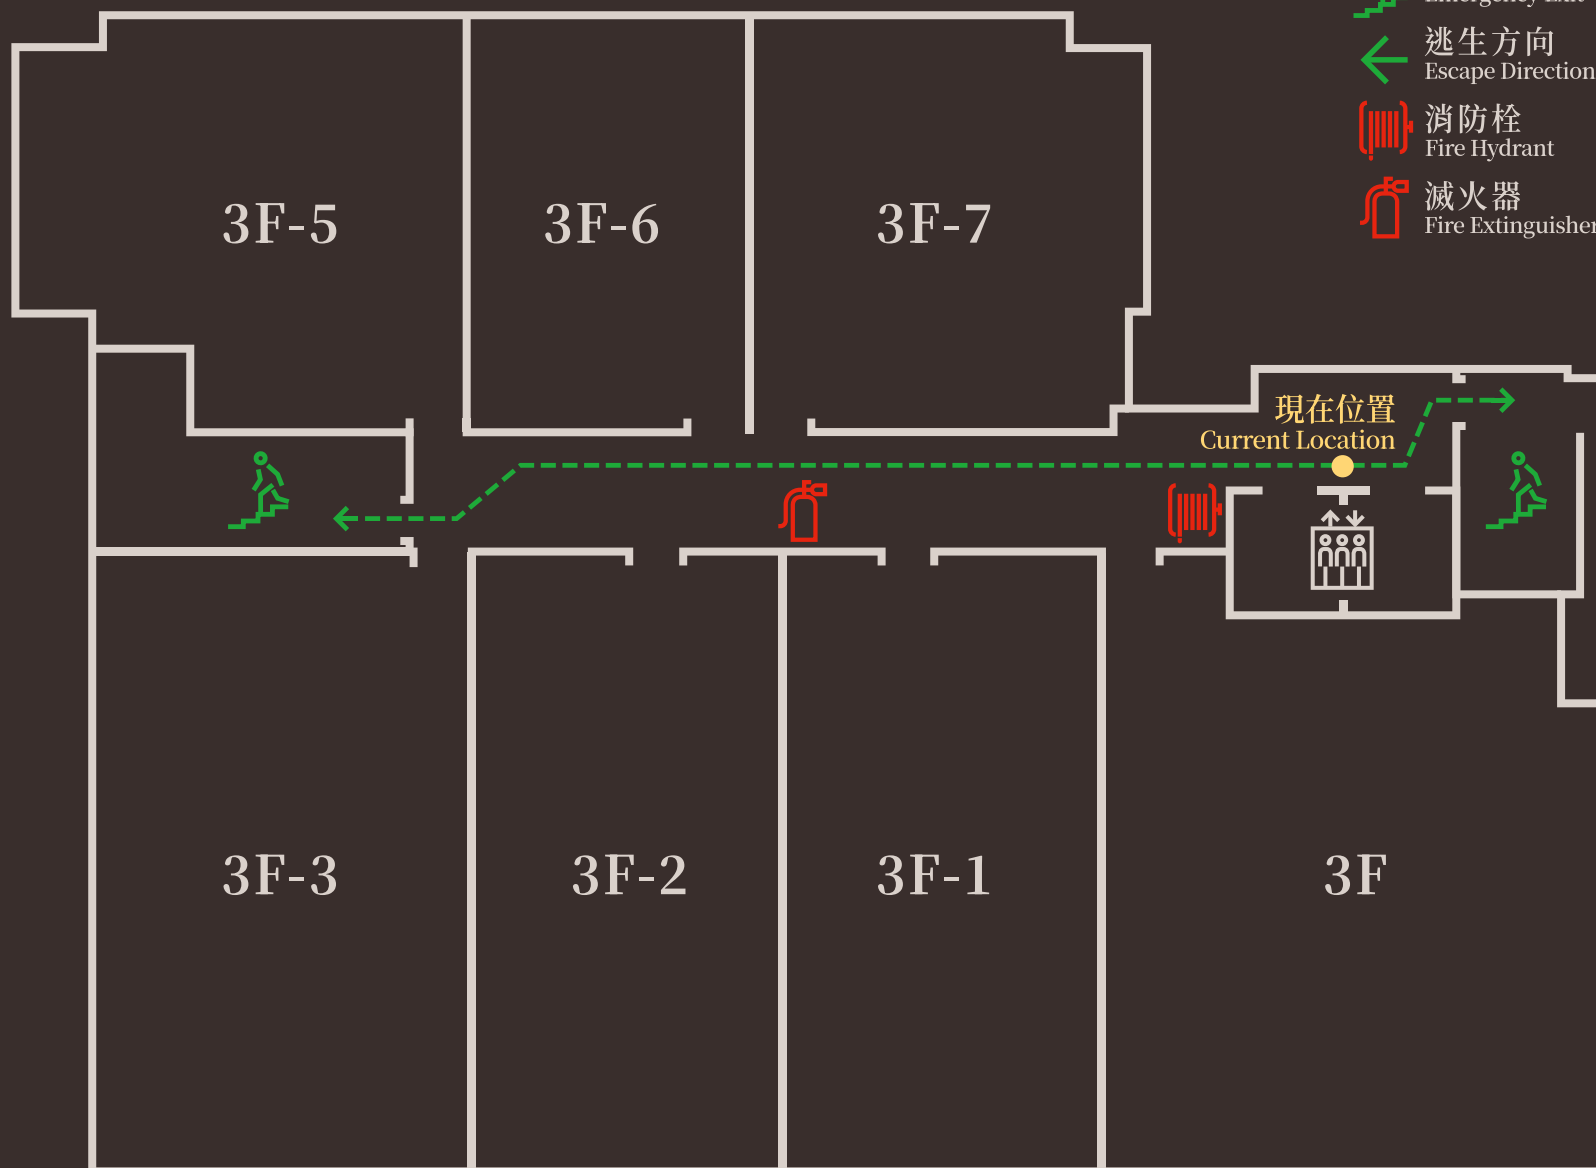


2F

緊急出口位置圖

Evacuation Plan


-  緊急出口
Emergency Exit
-  逃生方向
Escape Directions
-  消防栓
Fire Hydrant
-  滅火器
Fire Extinguisher

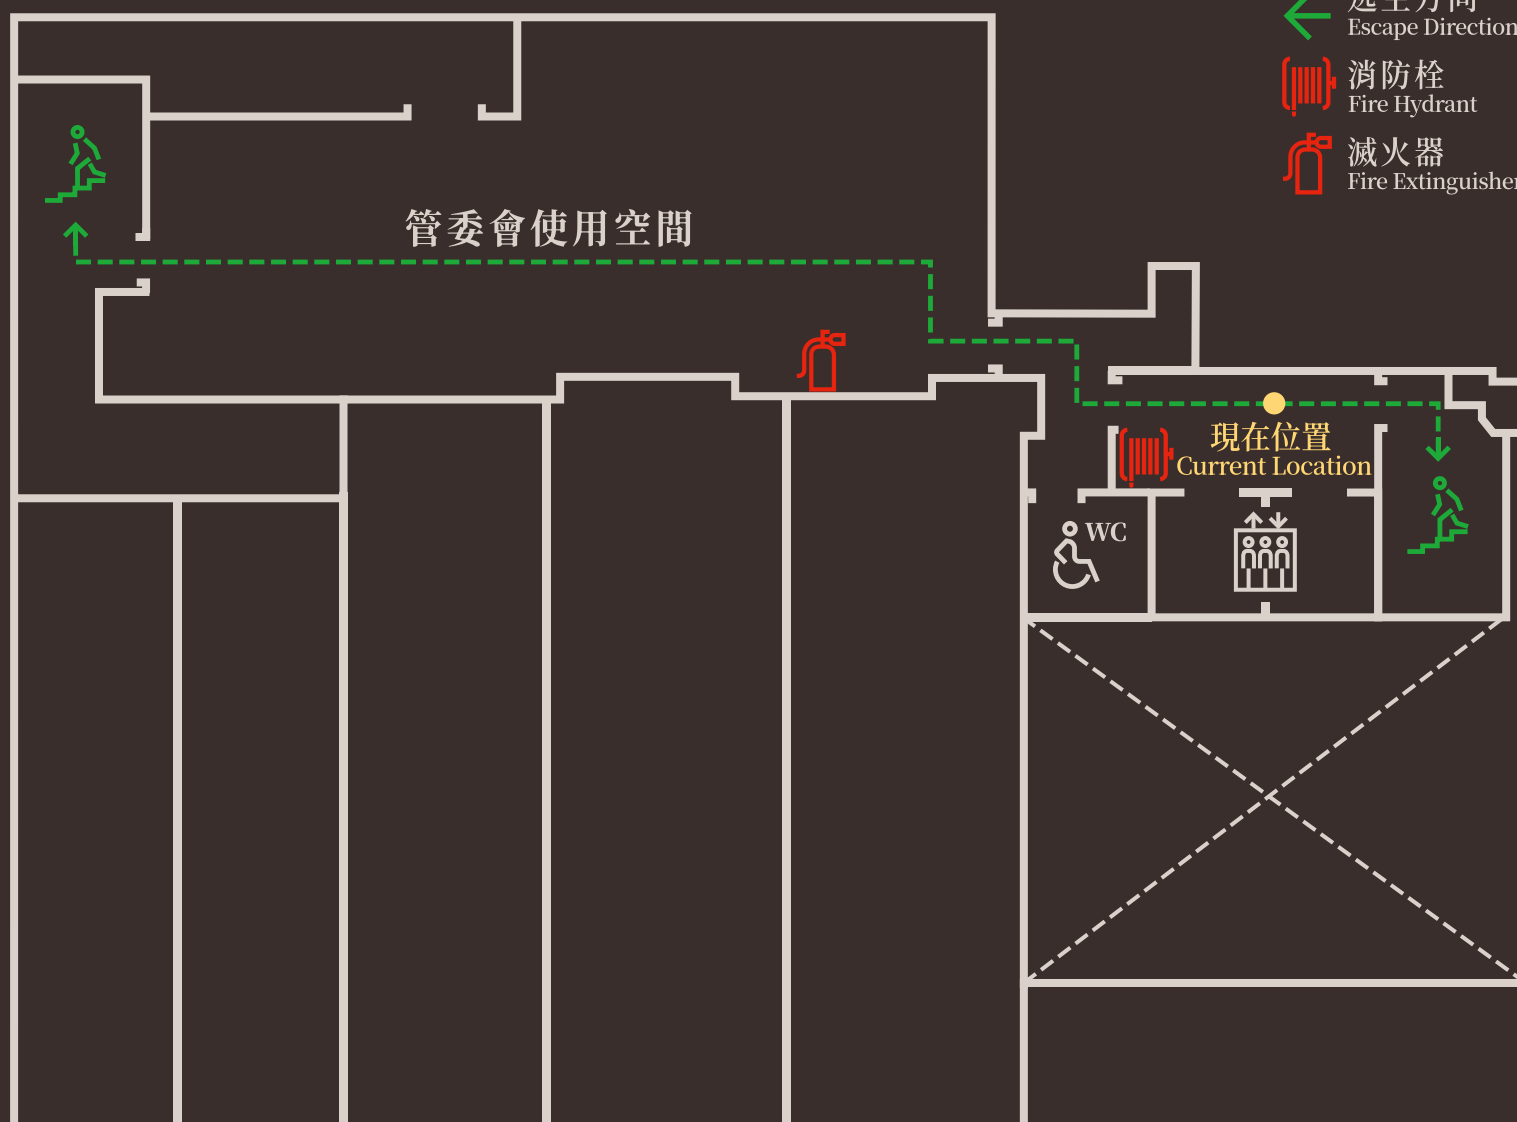

1F

緊急出口位置圖


Evacuation Plan

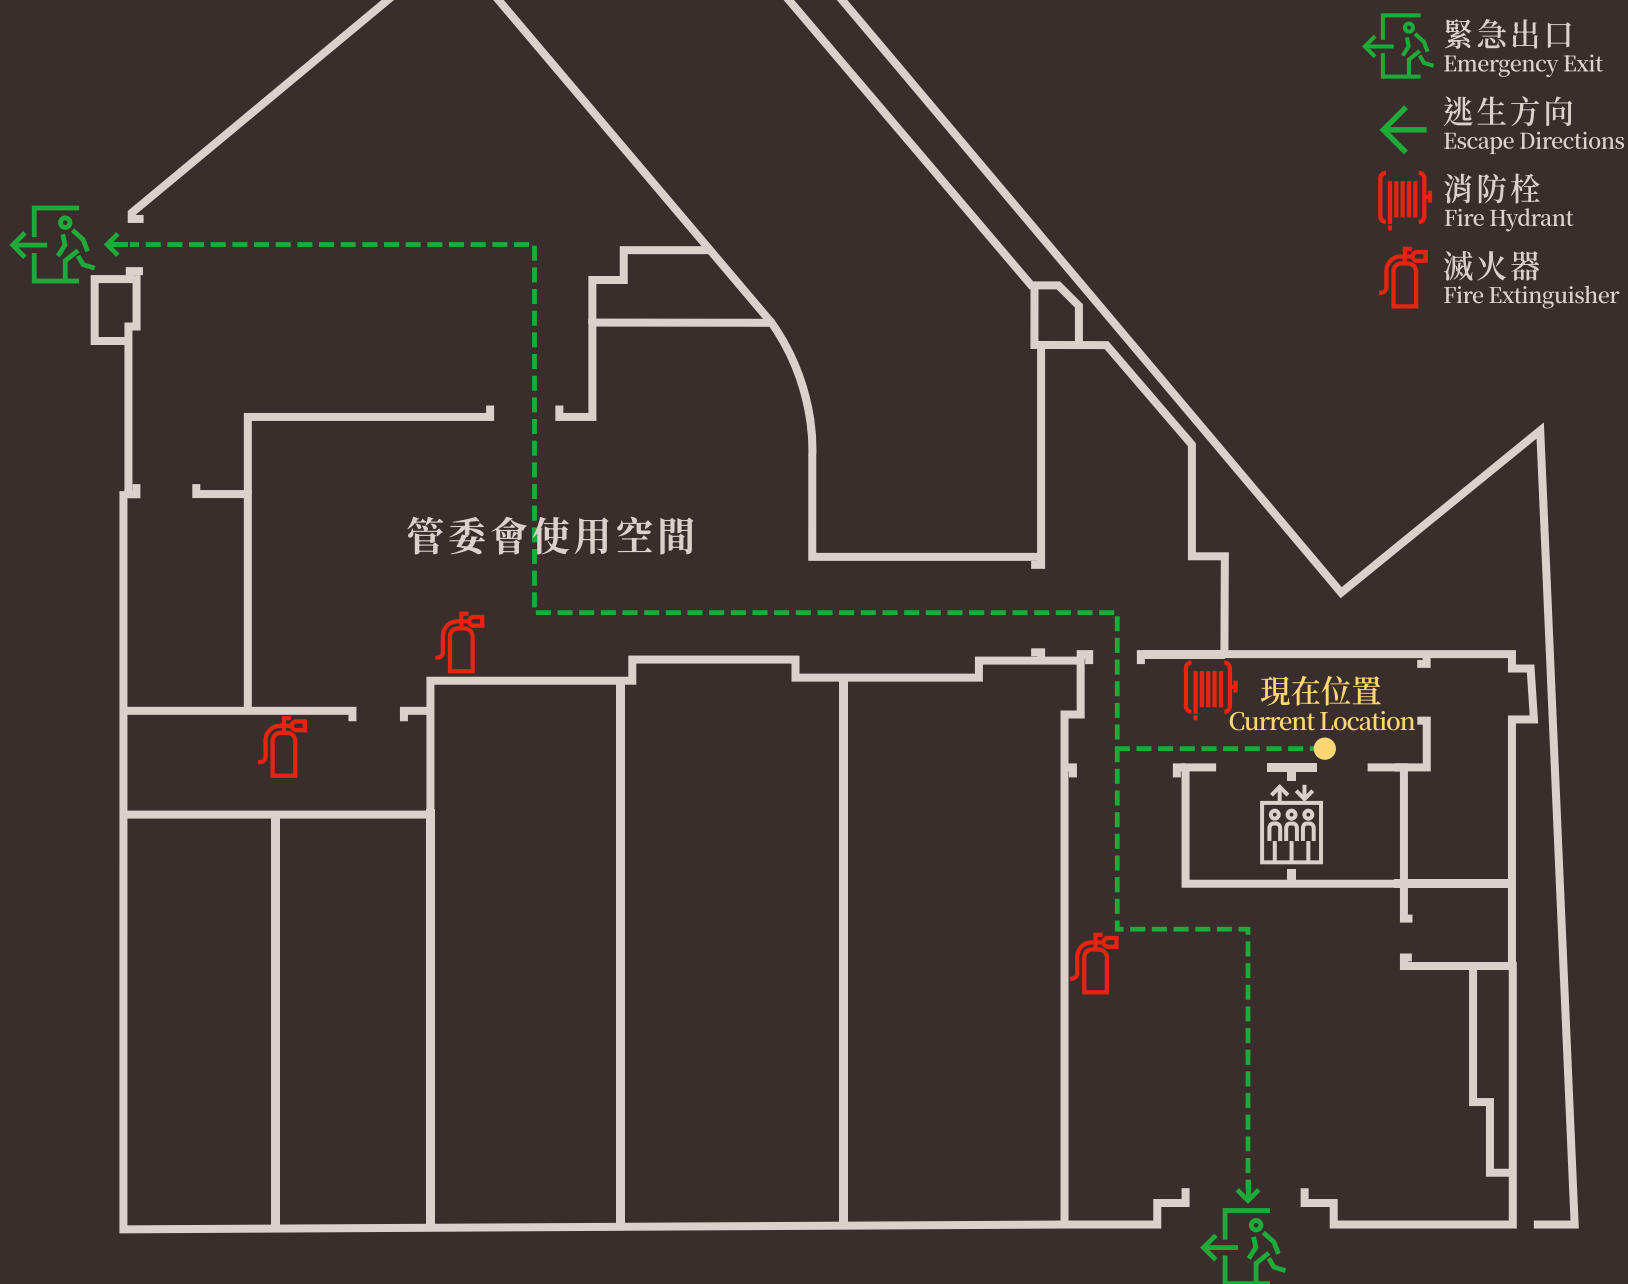

B1

緊急出口位置圖


Evacuation Plan

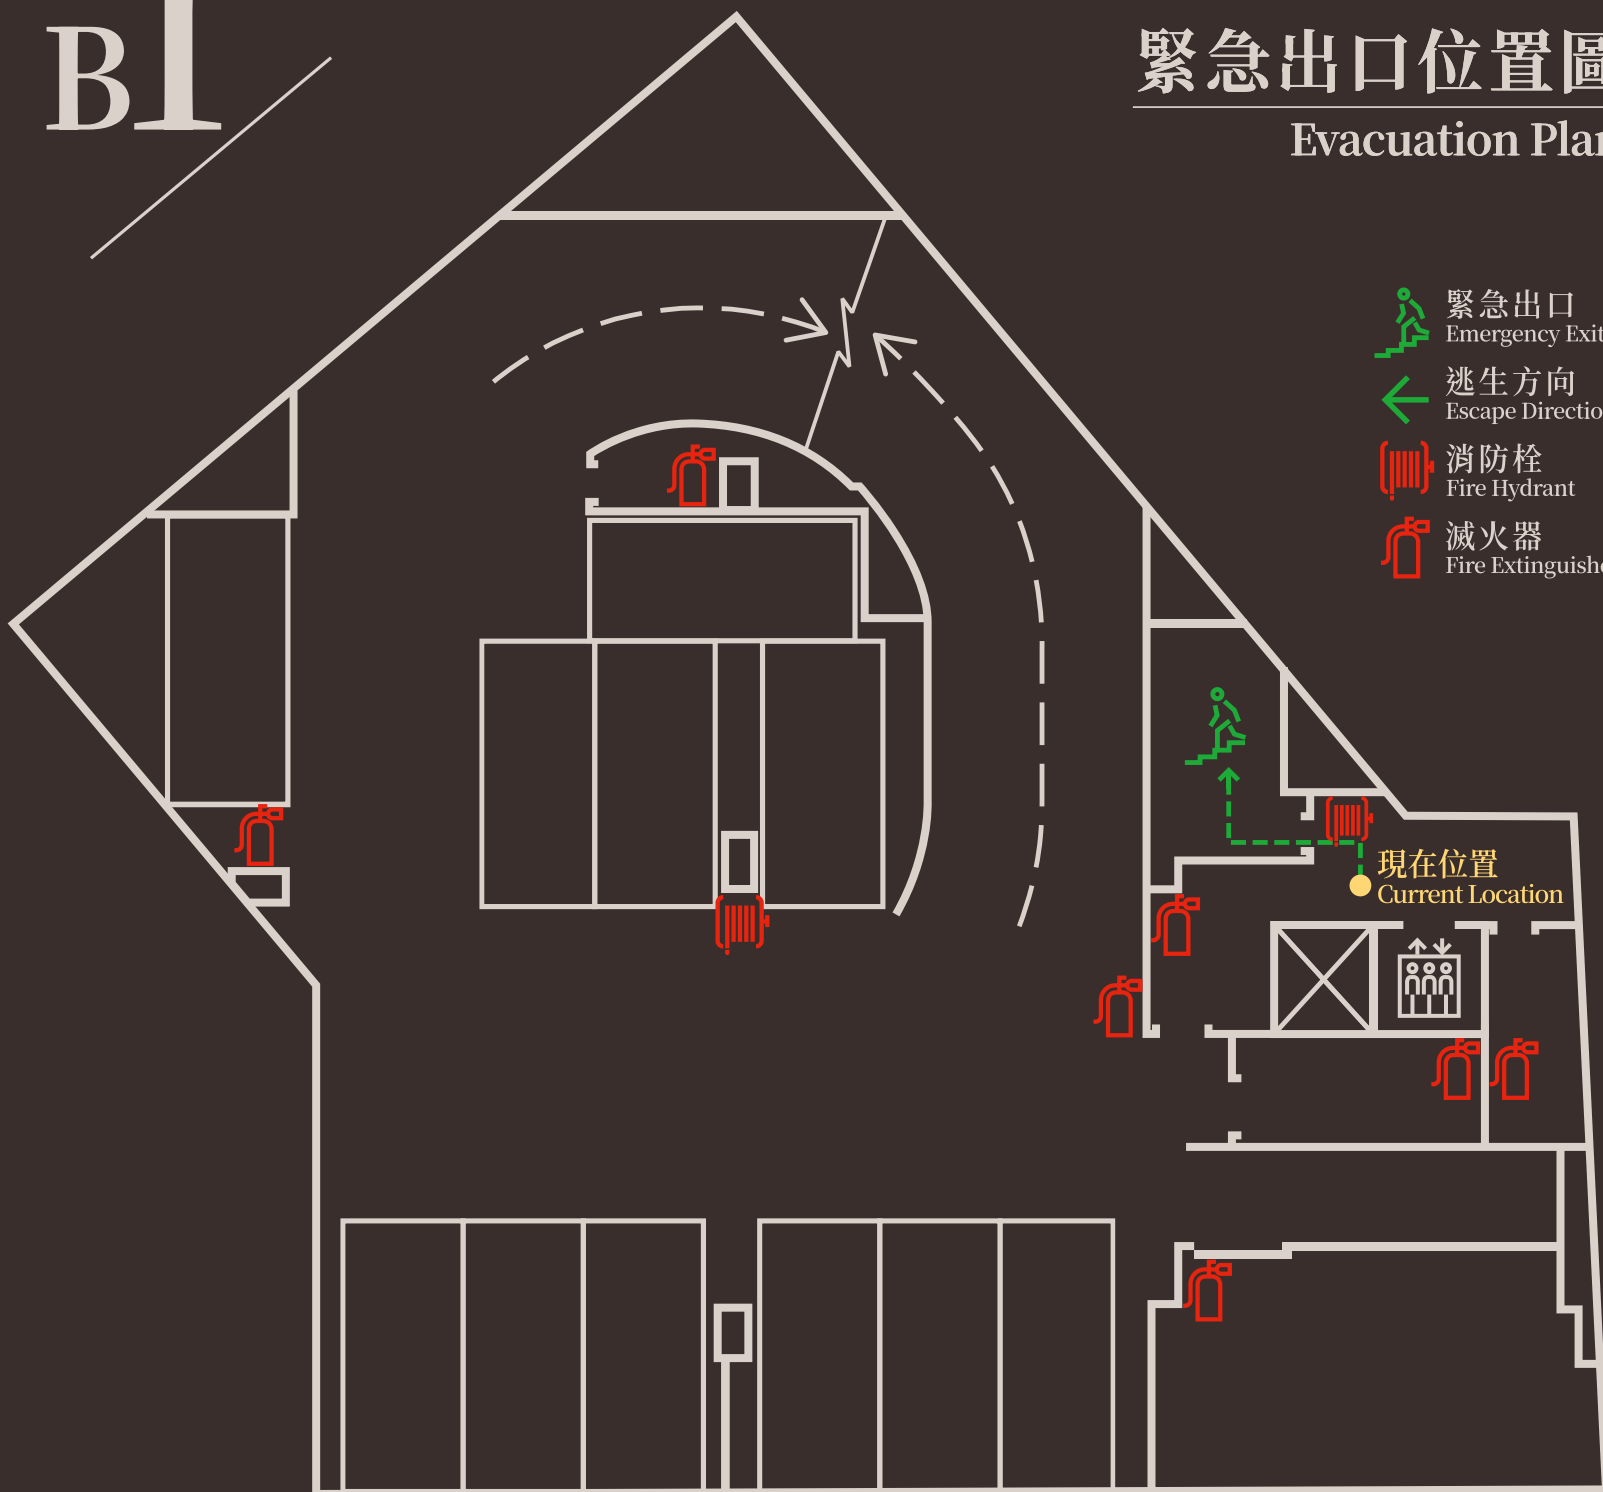

B2

緊急出口位置圖


Evacuation Plan

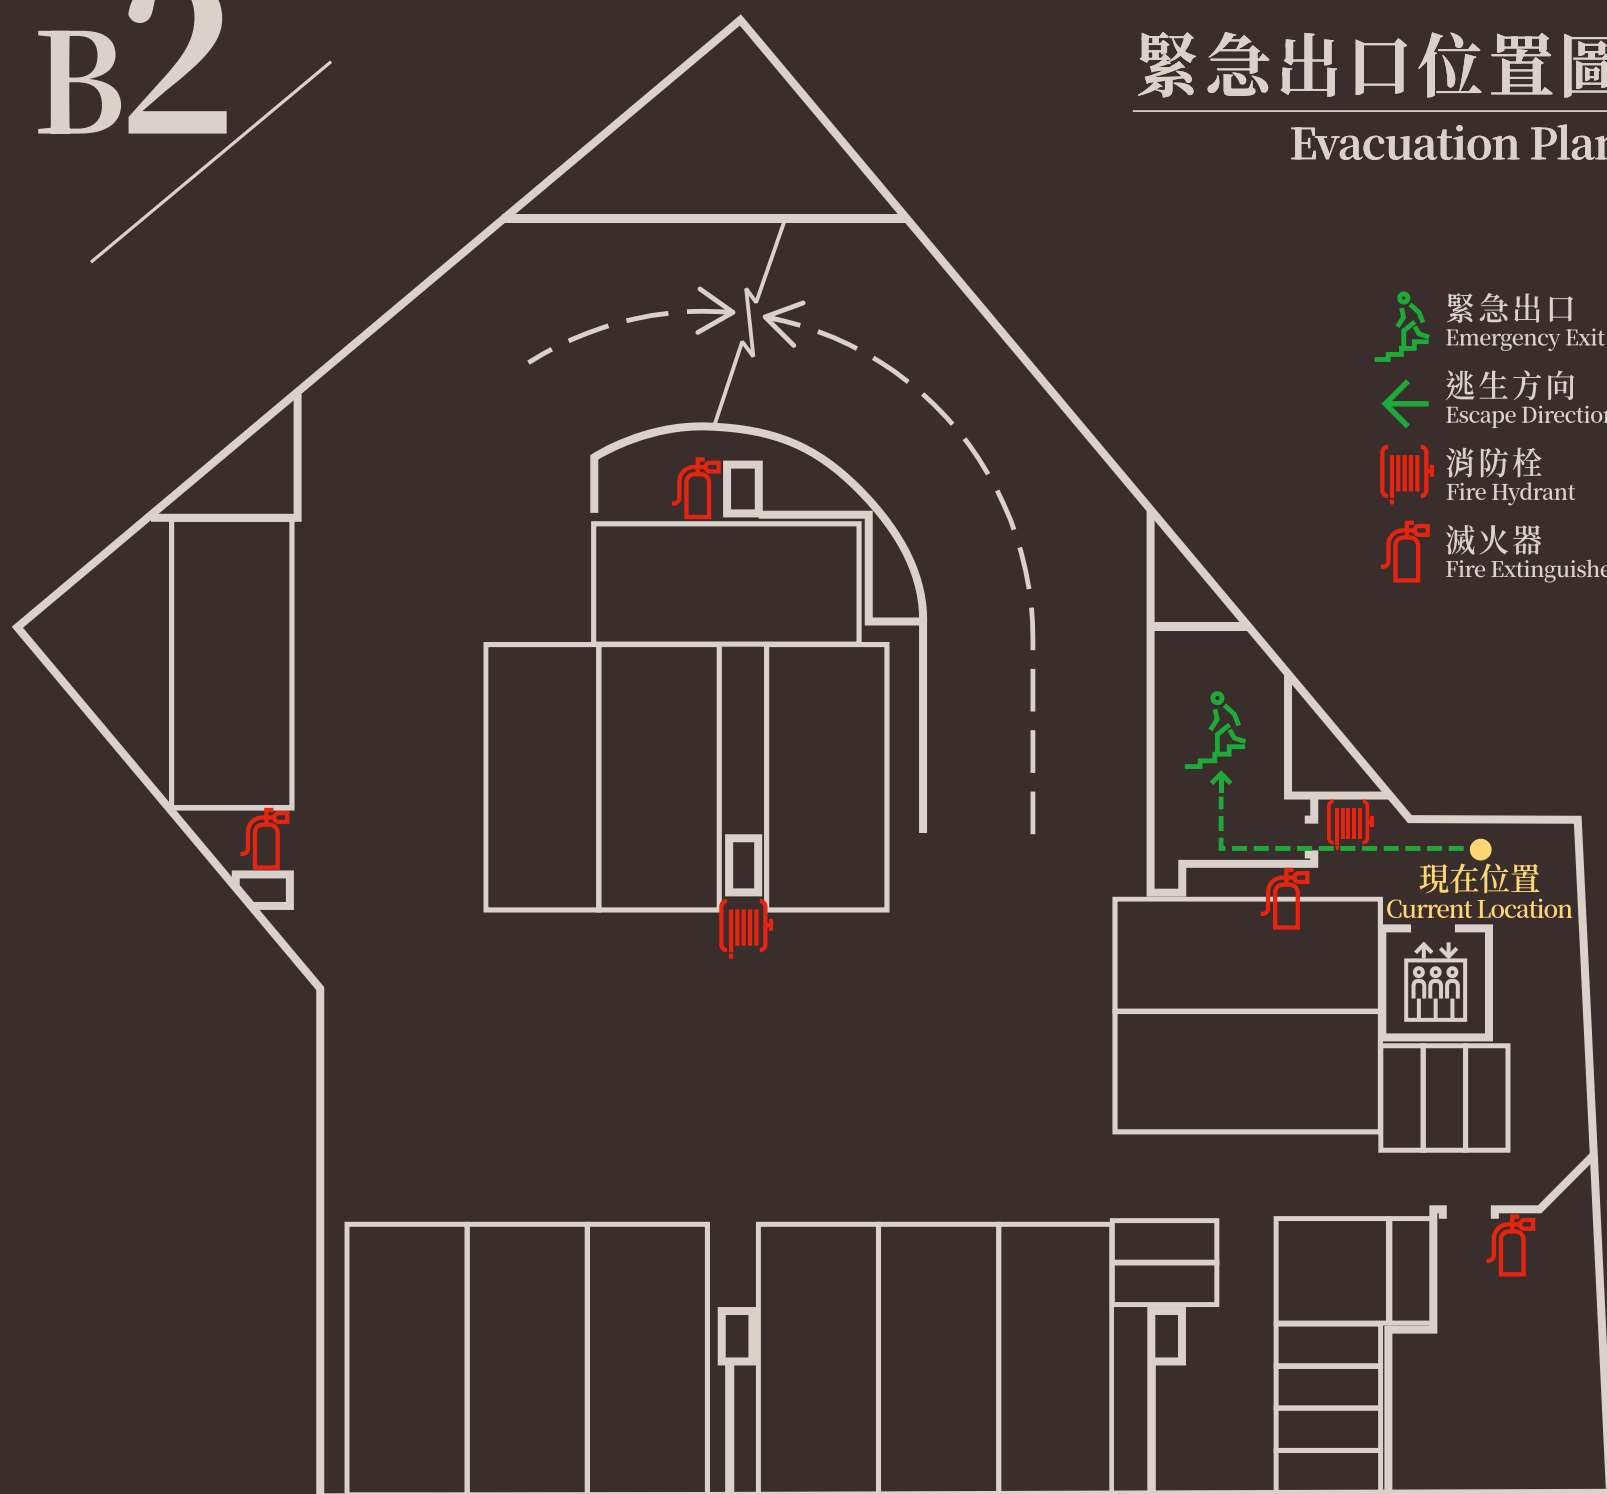

B3

緊急出口位置圖

Evacuation Plan

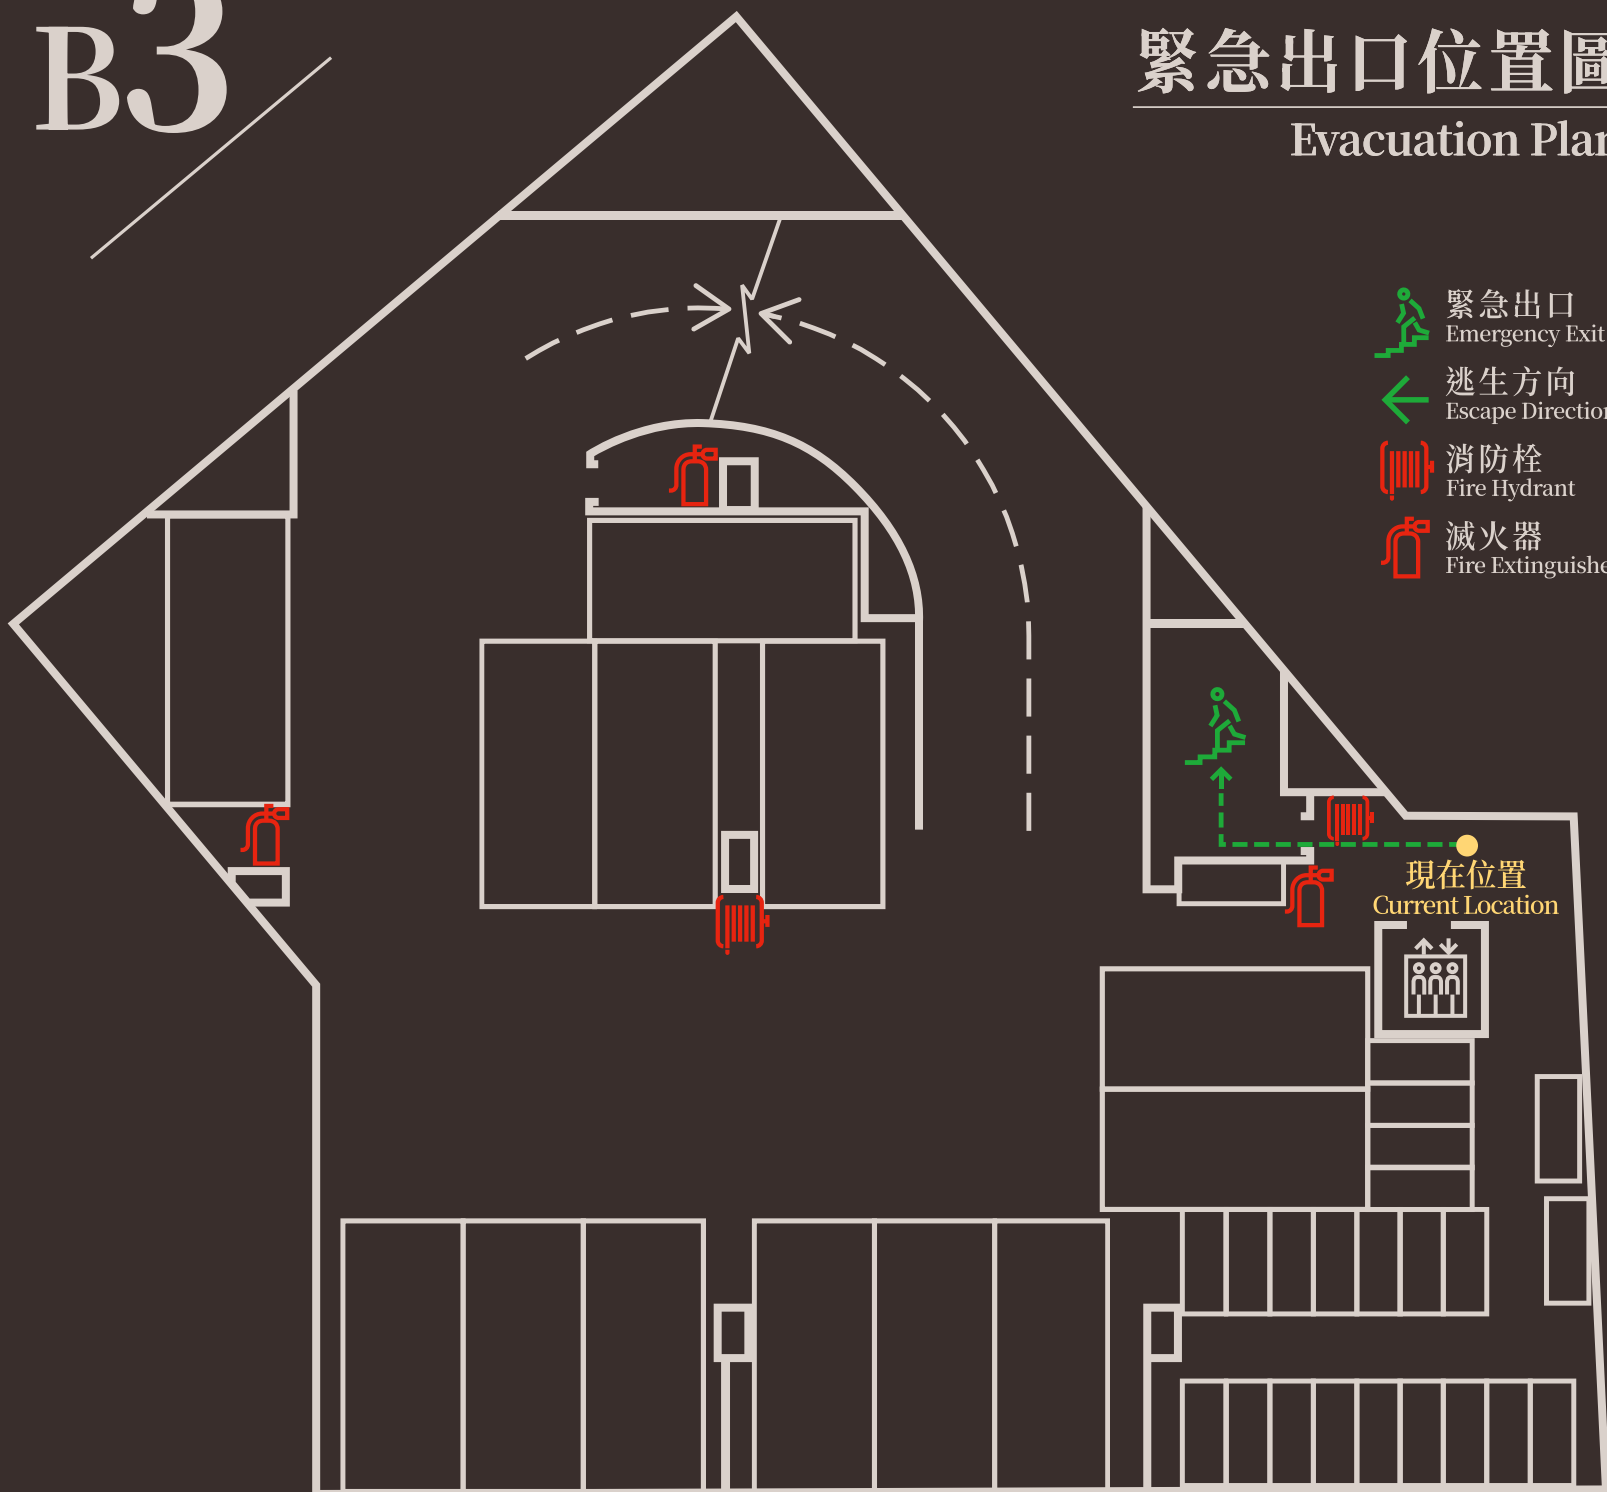

B4

緊急出口位置圖

Evacuation Plan

